



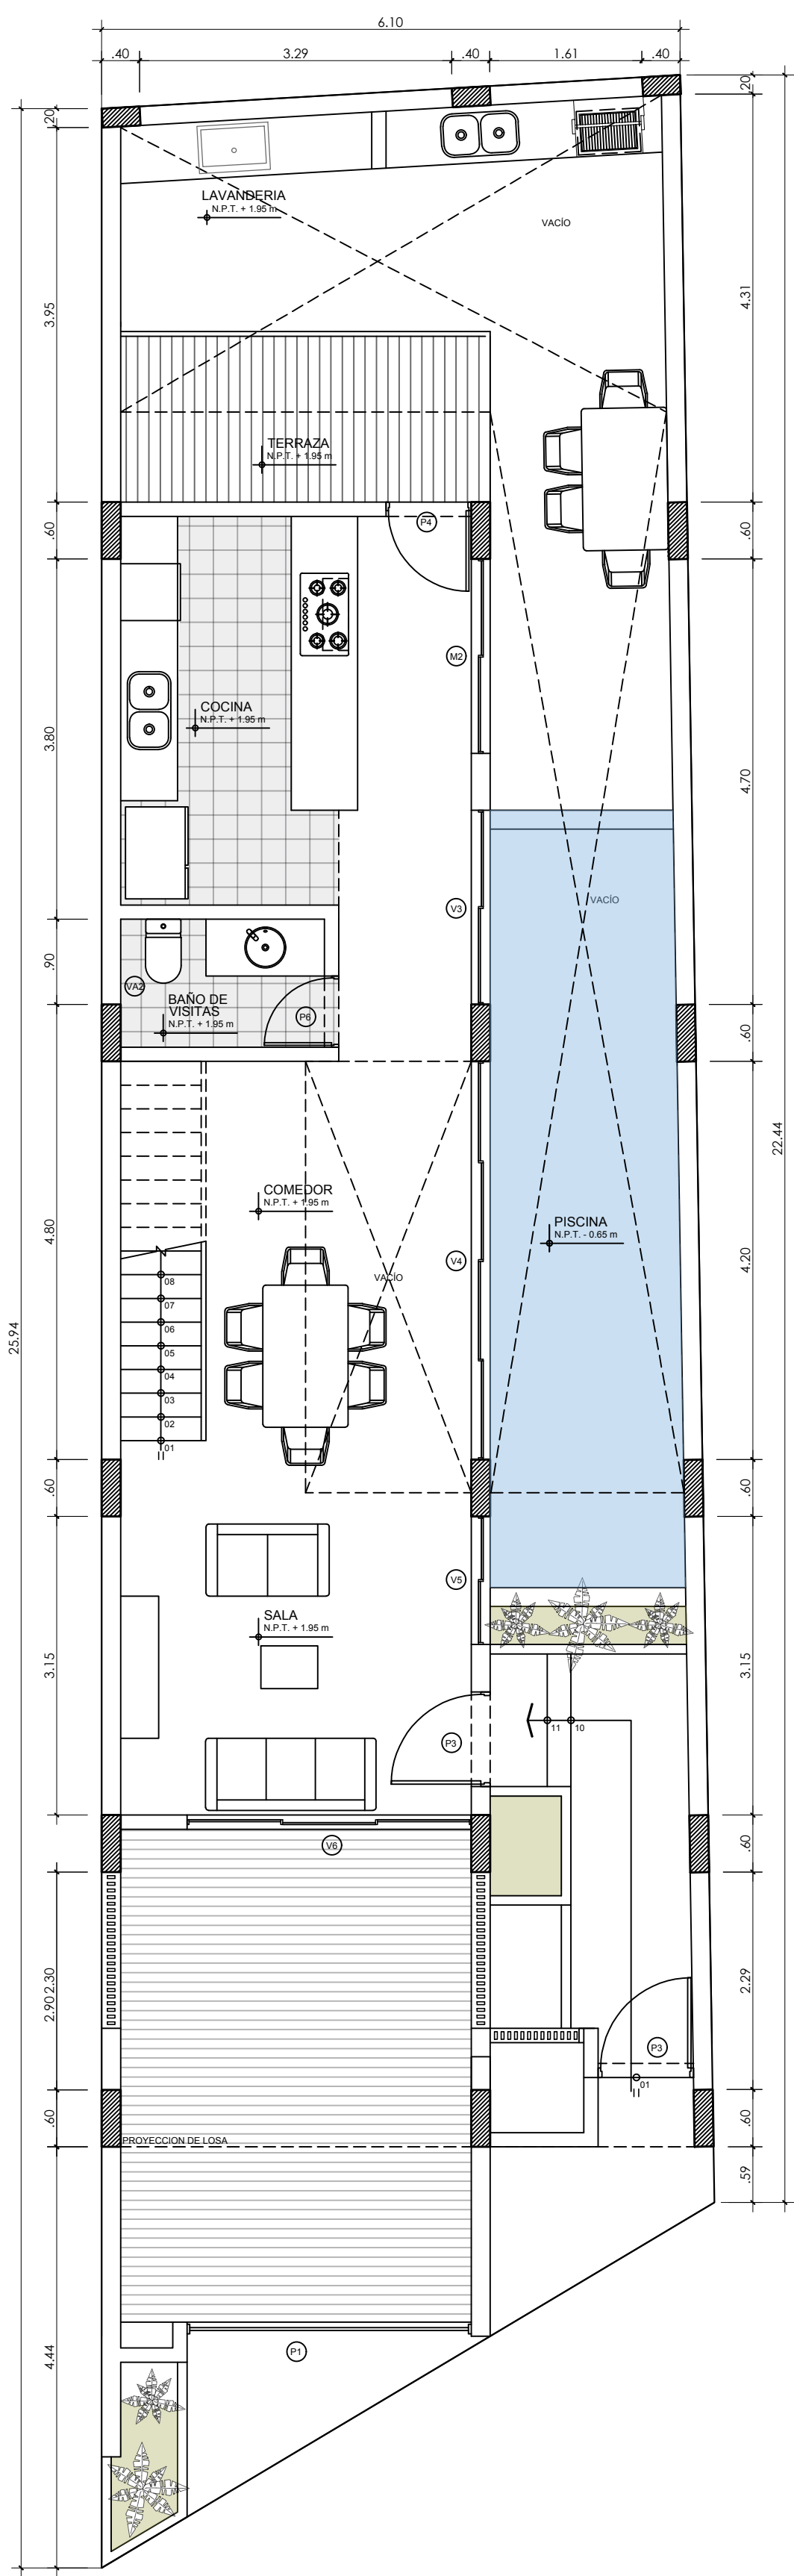


AREA TECHADA: 79.34 M2
PRIMER NIVEL
N.P.T. + 01.95 m


ÁREA TECHADA TOTAL: 249.57m2

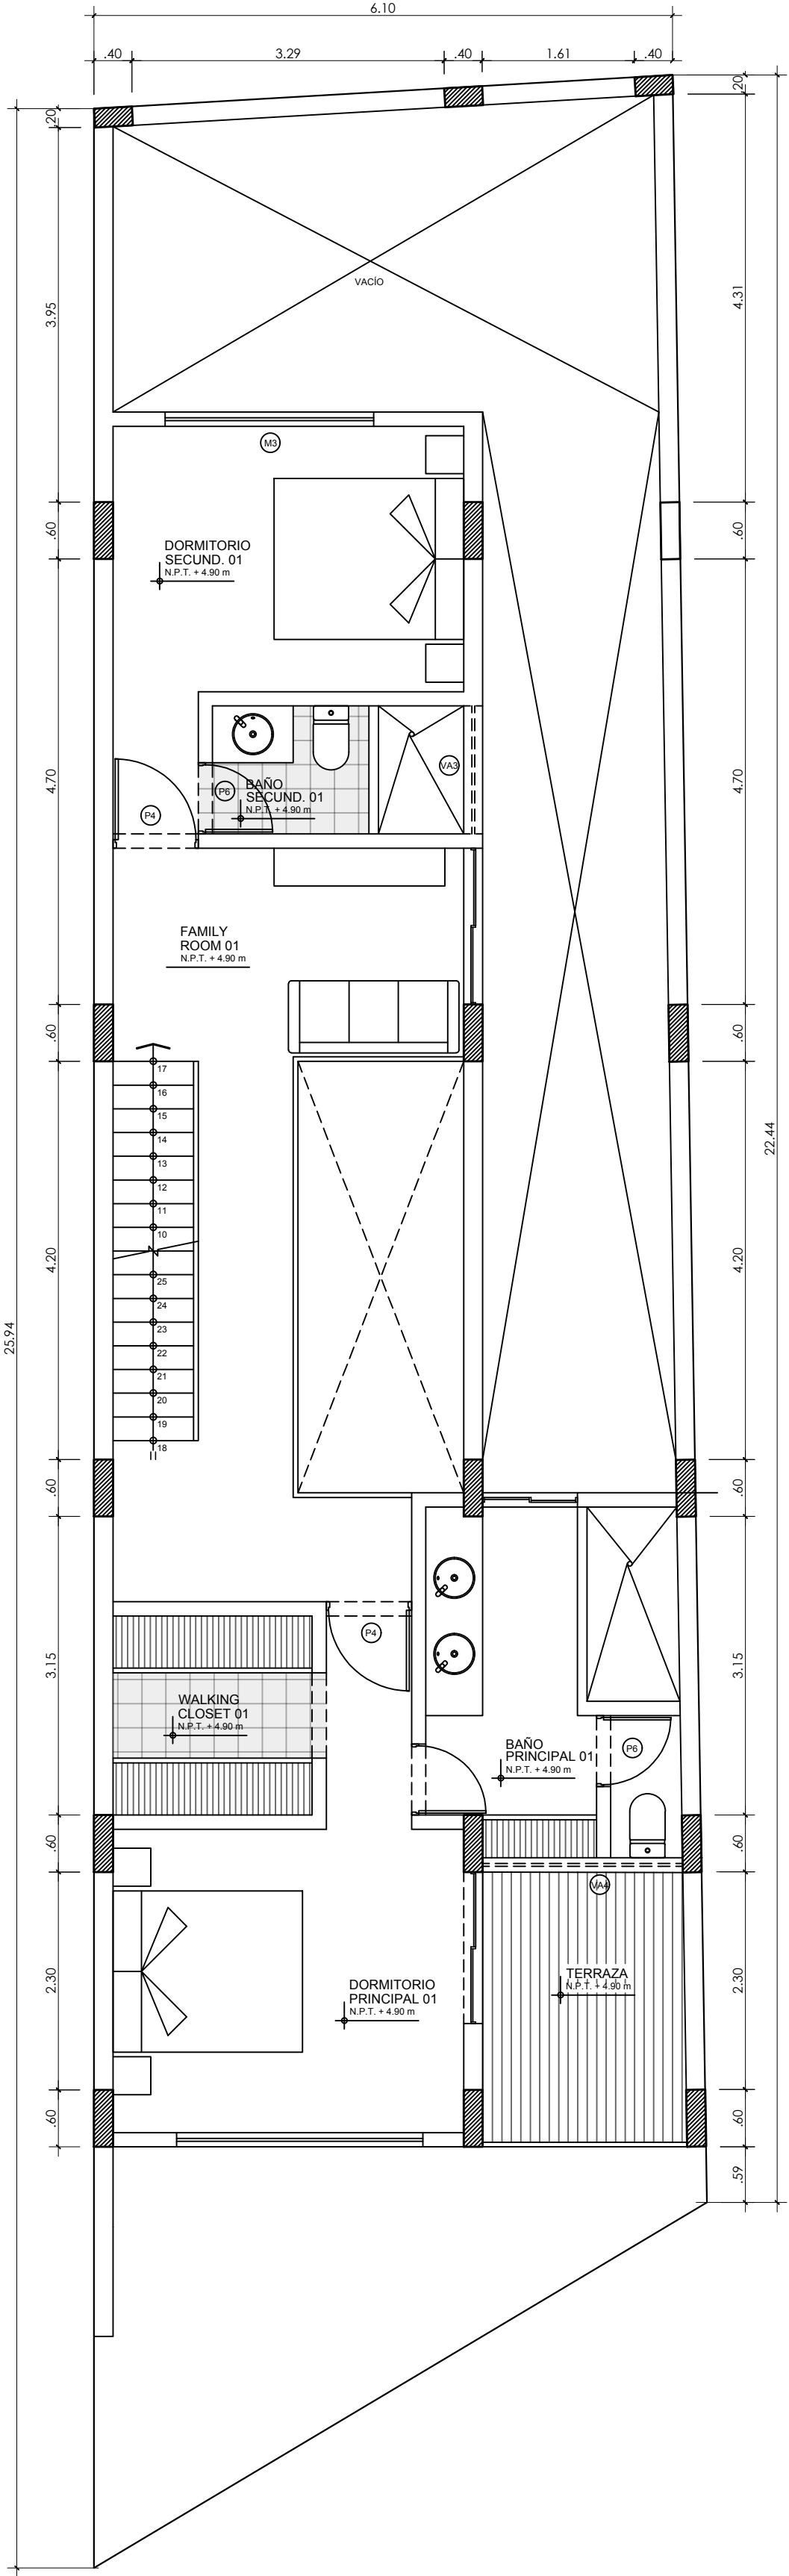


AREA TECHADA: 79.34 M2
SEGUNDO NIVEL
N.P.T. + 04.90 m

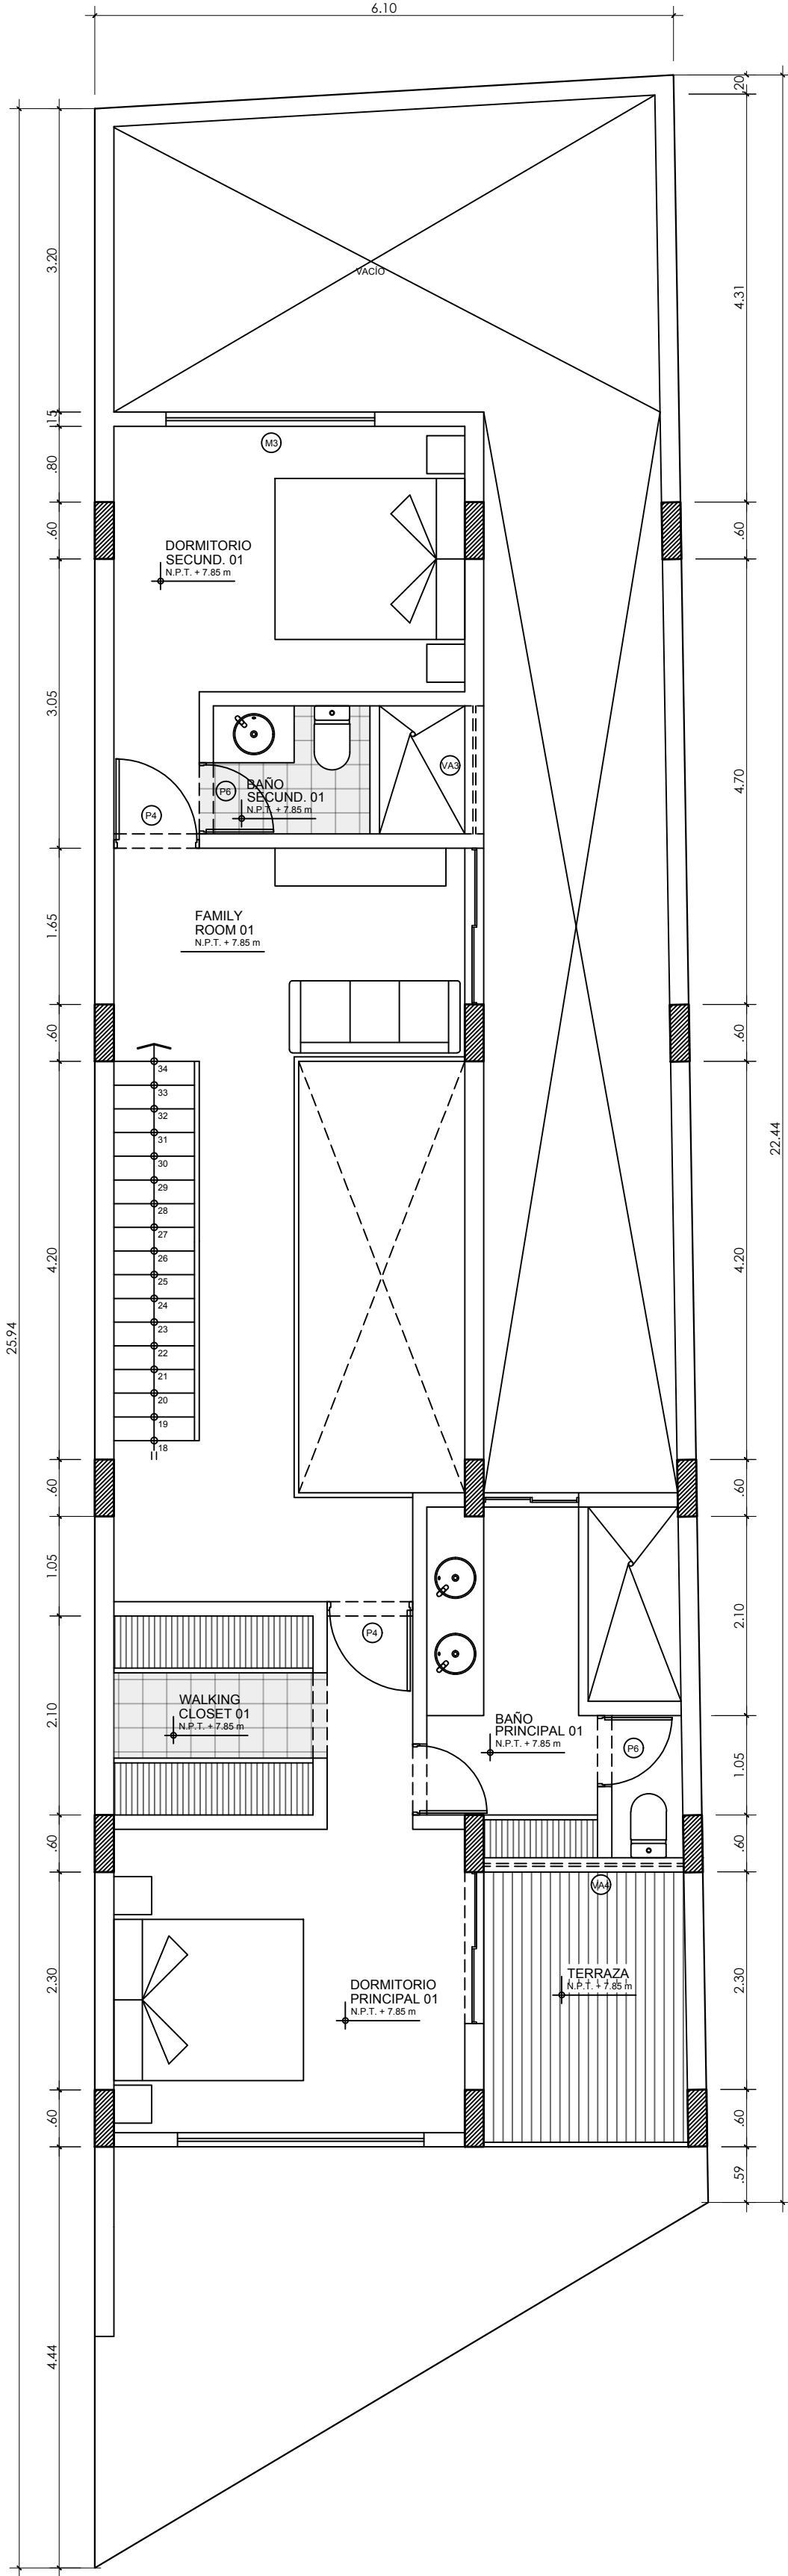

AREA TECHADA: 90.89 M2
TERCER NIVEL
N.P.T. + 07.85 m

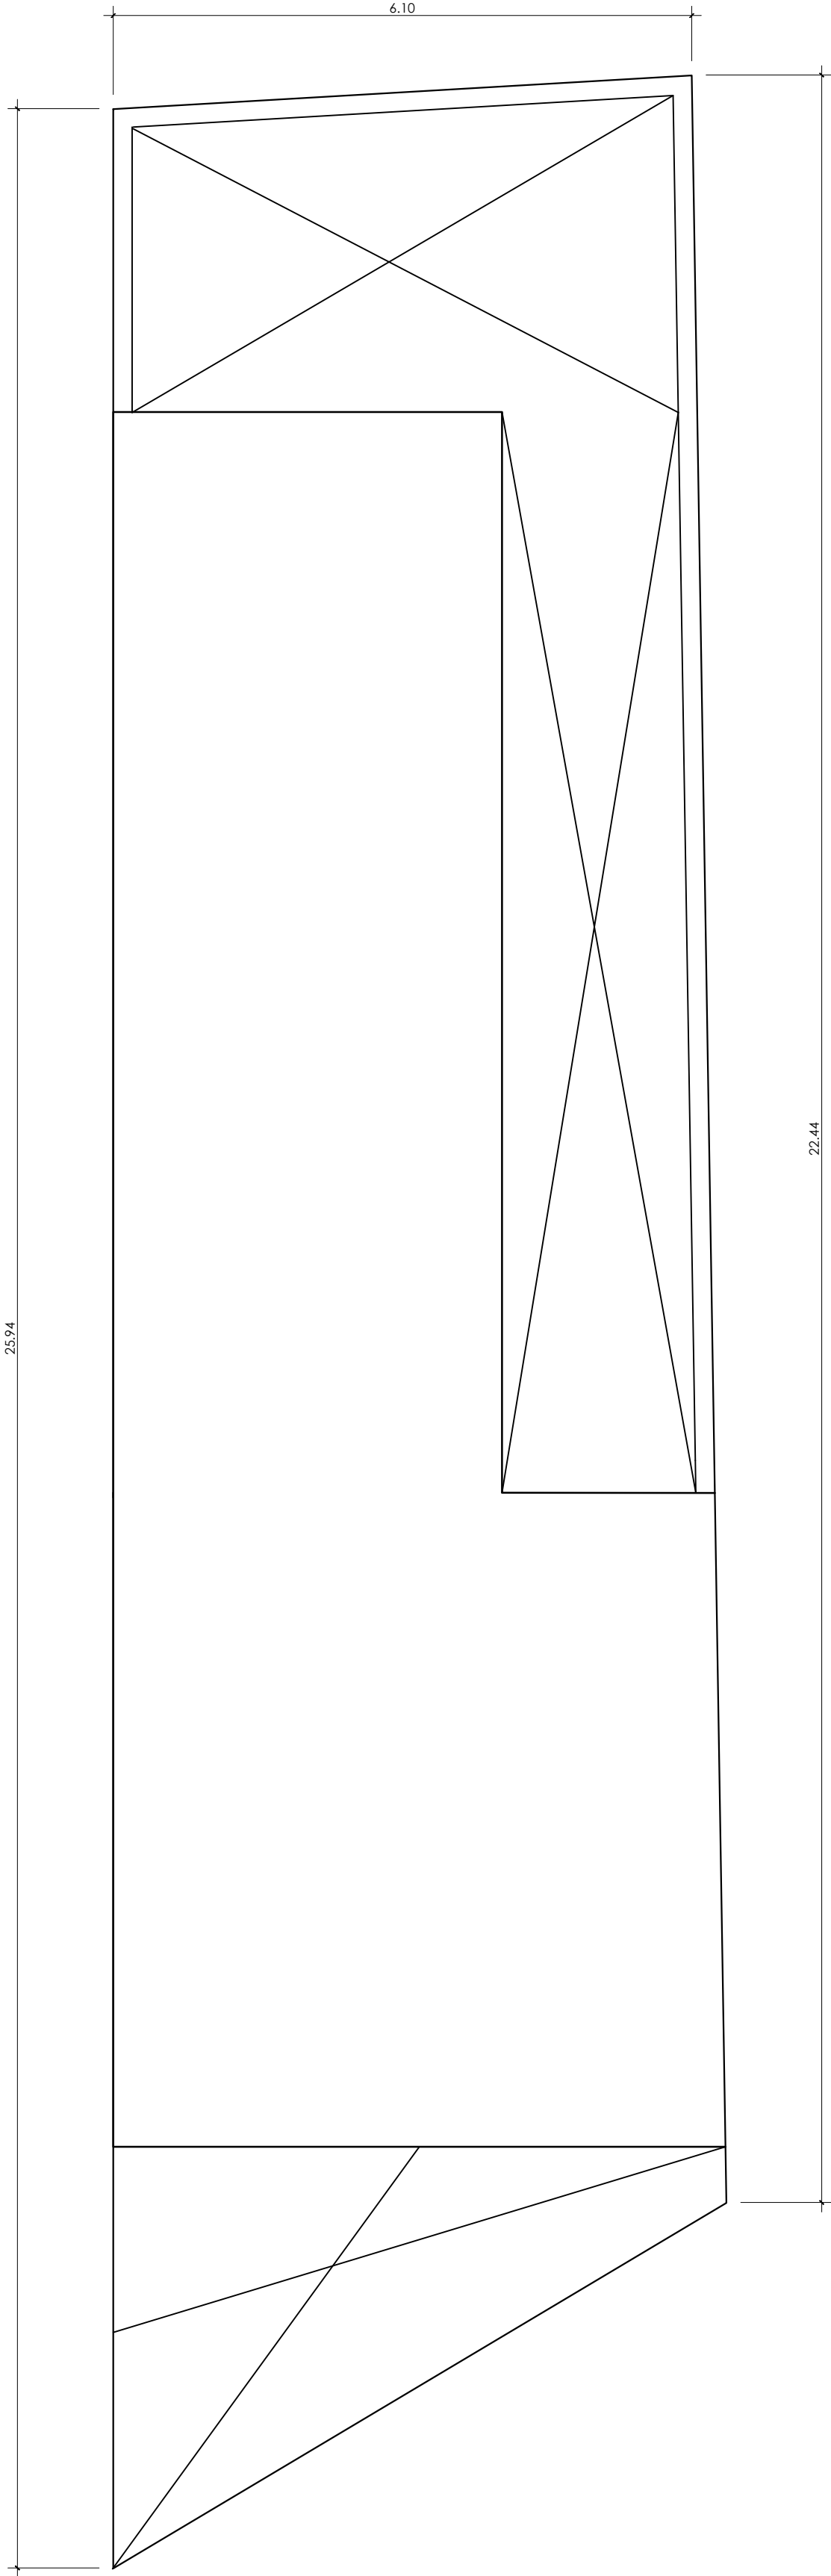

TECHO NIVEL

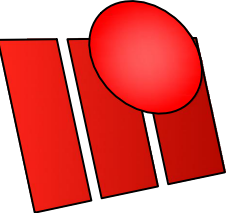

MP ARQUITECTURA Y CONSTRUCCIÓN SAC.
Arquitectura, Ingeniería y Construcción
Calle Alfonso Ugarte N° 838 - Of. 301 - Chiclayo - Perú.
Celular: 979 999 082 Email: mparquitecturayc@gmail.com

PROYECTO:
VIVIENDA UNIFAMILIAR

ESPECIALIDAD:
ARQUITECTURA
DESARROLLO DE PLANTAS

DESCRIPCION:
PRIMER, SEGUNDO Y TERCER NIVEL

PROPIETARIO:

Sr. XXXXXXXX
DNI XXXXXXXX

PROFESIONAL:

ARQ. MARIO EDUARDO PEREZ ANGULO
CAP - 3328

UBICACION:
URB. LOS NOGALES, MZ "W", LOTE 20

REGION	PROVINCIA	DISTRITO
LAMBAYEQUE	CHICLAYO	PIMENTEL
ESCALA: 1 / 50	FECHA: OCTUBRE 2022	DIBUJO: MP
LÁMINA: A-01		